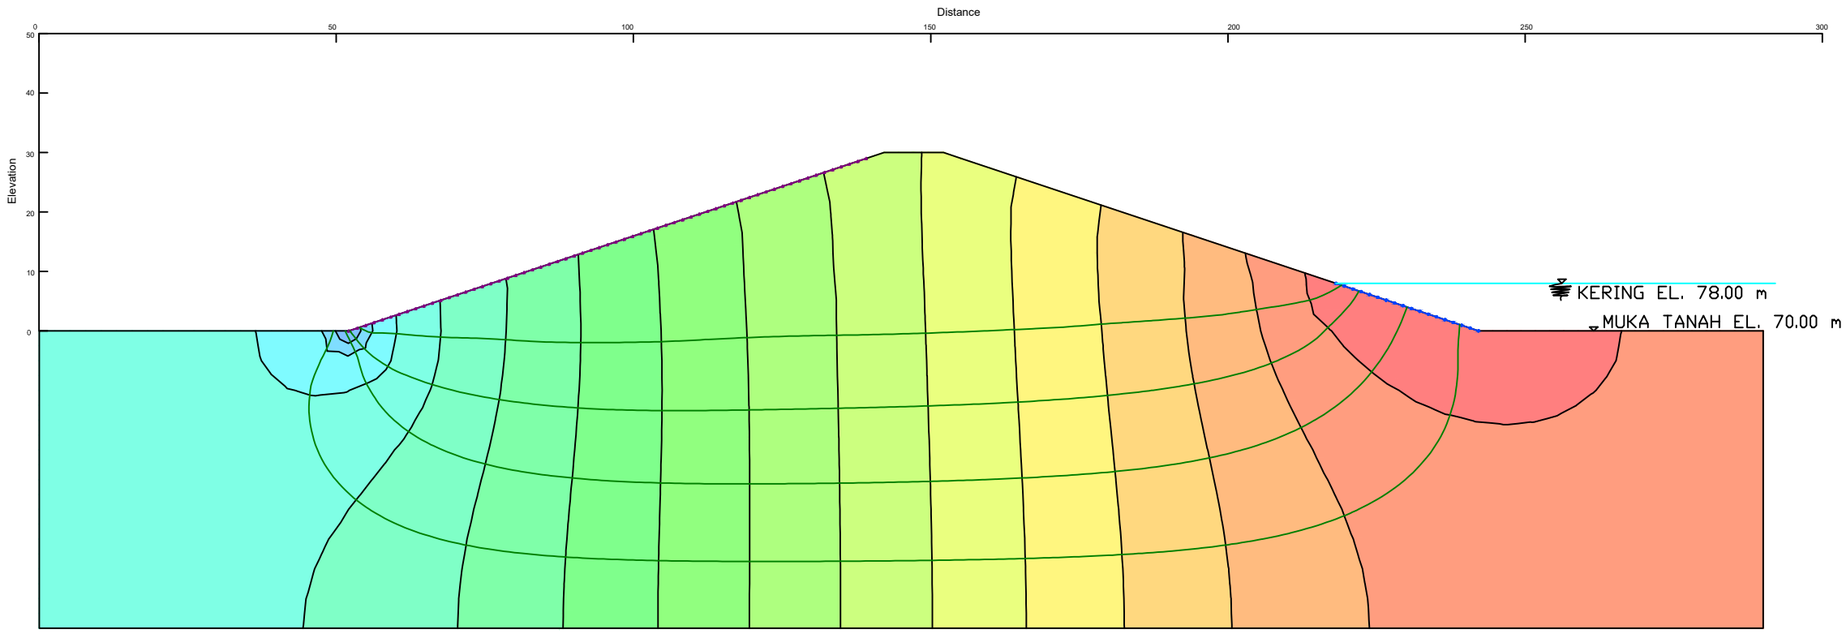

DEPARTEMEN TEKNIK
INFRASTRUKTUR SIPIL
FAKULTAS VOKASI
INSTITUT TEKNOLOGI SEPULUH
NOPEMBER

STABILITAS LERENG

DOWNSTREAM
RAPID
DROPDOWN

TYPE LERENG

LERENG TYPE 1

ANALISIS

FLOWNET

DOSEN

DERIS FAISA
RALINDRA, S.T., M.T.

MAHASISWA

DINA NABILA SARI
2036221078
TRKBA-D

NO. LEMBAR	NILAI
01	